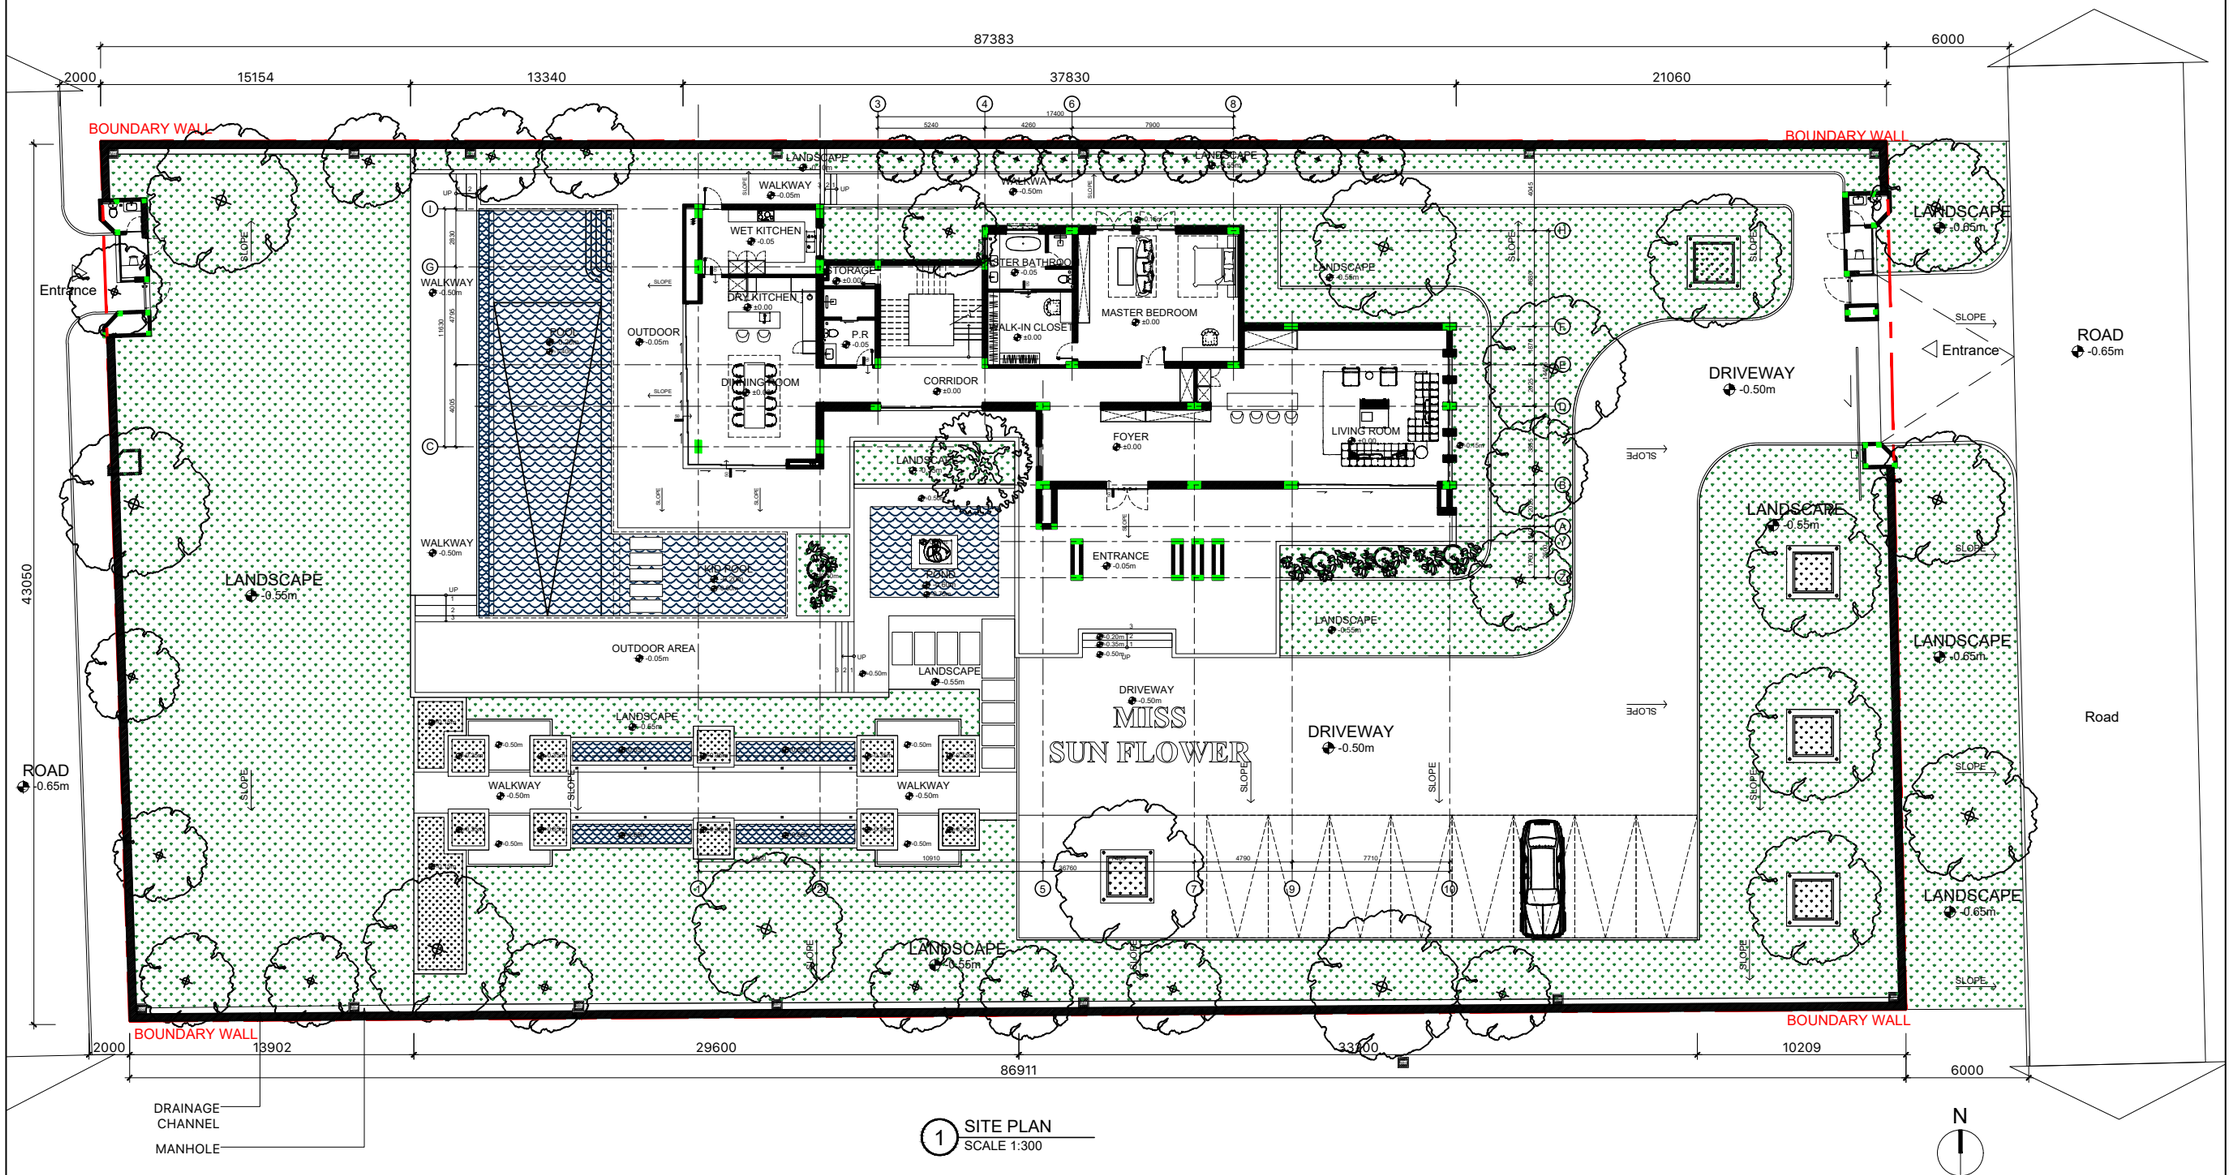


1 SITE PLAN
SCALE 1:300

TENDER
ISSUE
12-DEC-2024

PROJECT:
OWNER:

ADDRESS:
TEL. :

ARCHITECT

STRUCTURE ENGINEER

MEP ENGINEER

GENERAL NOTE:
1. THIS DRAWING AND ANY SPECIFICATION THAT MAY ACCOMPANY IT ARE THE PROPERTY OF THE ARCHITECT, ENGINEER AND/OR OTHER CONSULTANTS HEREWITH LISTED AND MUST NOT BE REPRODUCED IN ANY FORM, WHETHER IN WHOLE OR IN PART, WITHOUT THE EXPRESSED WRITTEN PERMISSION OF THE OWNERS.
2. ALL ARCHITECTURAL, STRUCTURAL, MECHANICAL/ELECTRICAL, INTERIOR, LANDSCAPE AND LIGHTING DESIGN DRAWINGS SHOWN ARE FOR DESIGN INTENT ONLY. CONTRACTOR TO PROVIDE DETAILED SHOP DRAWINGS FOR ARCHITECT'S AND/OR ENGINEER'S APPROVAL PRIOR TO CONSTRUCTION.
3. ON NO ACCOUNT MAY THIS DRAWINGS BE SCALED, ANY DISCREPANCY IN FIGURED DIMENSIONS (OR OTHERWISE DISCREPANCIES BETWEEN ARCHITECTURAL/STUCTURAL AND MECANICAL/ELECTRICAL DRAWINGS) IS TO BE REPORTED IMMEDIATELY TO THE ARCHITECT AND/OR ENGINEER BEFORE COMMENCEMENT OF WORKS.
4. CONSTRUCTORS MUST CHECK ALL DIMENSIONS FROM SITE.

REV.	DESCRIPTION	ISSUE DATE	INITIAL

DESIGN & DRAWN BY:
HENG THOURIN
LY VANPANHAPICH
TAING LEANGHOUT

PLOT DATE
12-Dec-24

SCALE
AS NOTED

REVISION


ISSUE STATUS
TD

PROJECT
SR VILLA

PROJECT NUMBER
016

DRAWING NAME
SITE PLAN

DRAWING NUMBER
10-01

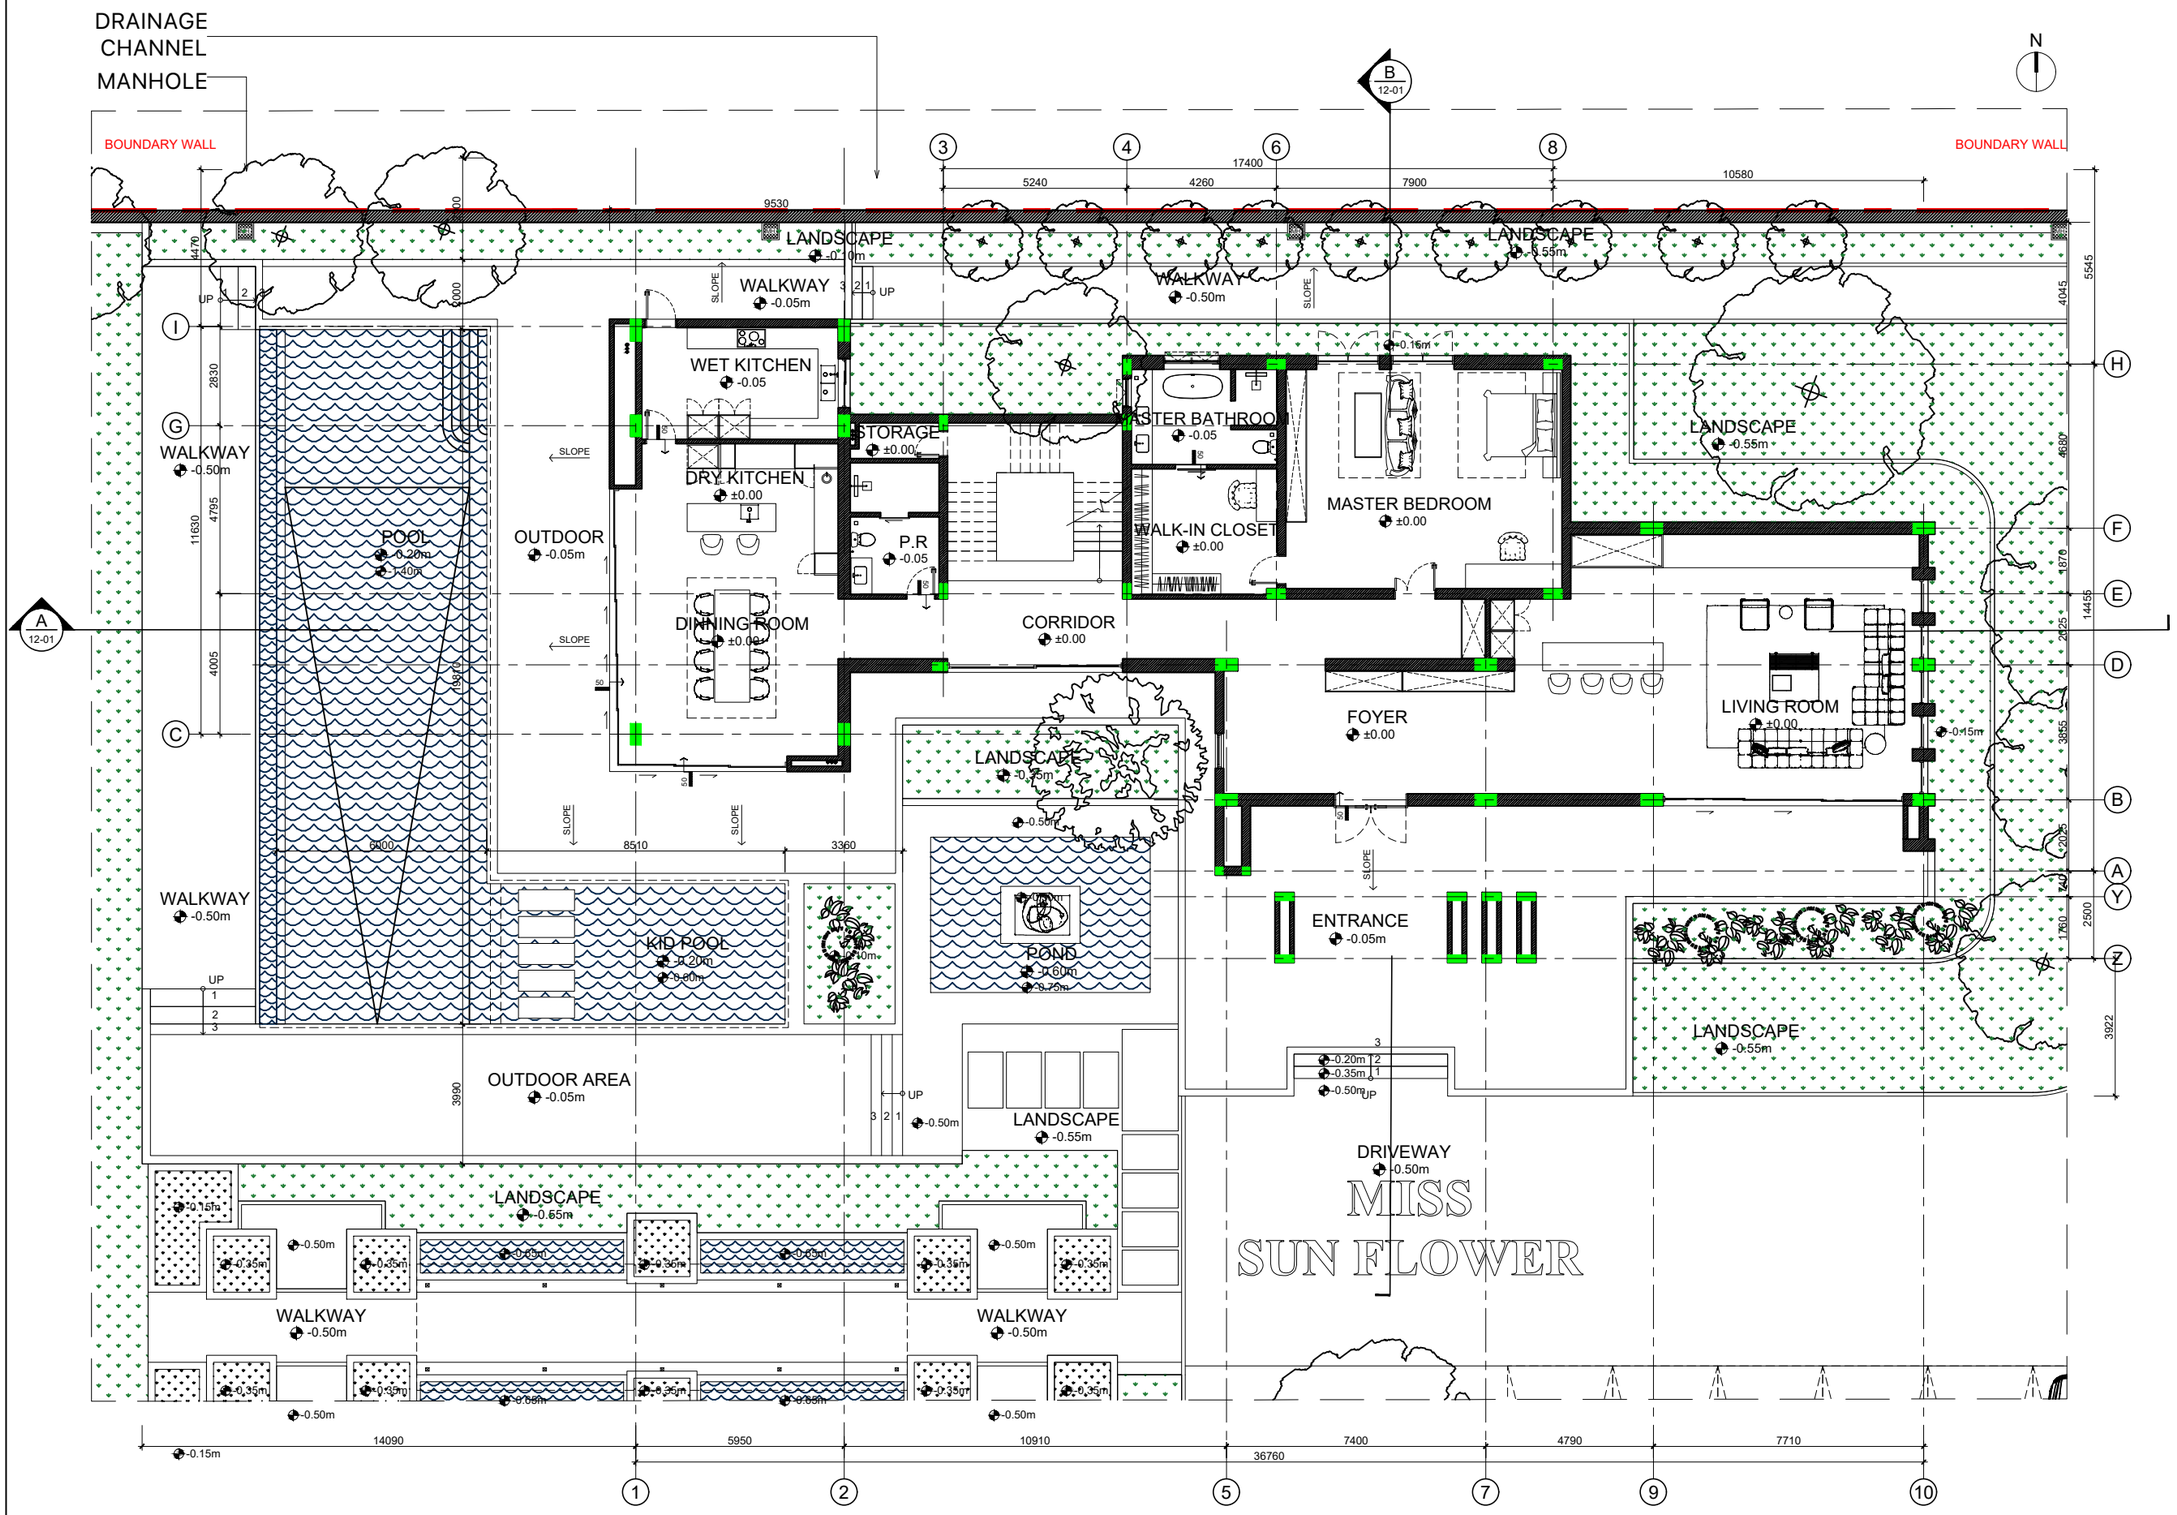

1 GROUND FLOOR PLAN
SCALE 1:175

TENDER
ISSUE
12-DEC-2024

PROJECT:
OWNER:

ADDRESS:
TEL. :

ARCHITECT

STRUCTURE ENGINEER

MEP ENGINEER

GENERAL NOTE:
1. THIS DRAWING AND ANY SPECIFICATION THAT MAY ACCOMPANY IT ARE THE PROPERTY OF THE ARCHITECT, ENGINEER AND/OR OTHER CONSULTANTS HEREWITH LISTED AND MUST NOT BE REPRODUCED IN ANY FORM, WHETHER IN WHOLE OR IN PART, WITHOUT THE EXPRESSED WRITTEN PERMISSION OF THE OWNERS.
2. ALL ARCHITECTURAL, STRUCTURAL, MECHANICAL/ELECTRICAL, INTERIOR, LANDSCAPE AND LIGHTING DESIGN DRAWINGS SHOWN ARE FOR DESIGN INTENT ONLY. CONTRACTOR TO PROVIDE DETAILED SHOP DRAWINGS FOR ARCHITECT'S AND/OR ENGINEER'S APPROVAL PRIOR TO CONSTRUCTION.
3. ON NO ACCOUNT MAY THIS DRAWINGS BE SCALED, ANY DISCREPANCY IN FIGURED DIMENSIONS (OR OTHERWISE DISCREPANCIES BETWEEN ARCHITECTURAL/STUCTURAL AND MECANICAL/ELECTRICAL DRAWINGS) IS TO BE REPORTED IMMEDIATELY TO THE ARCHITECT AND/OR ENGINEER BEFORE COMMENCEMENT OF WORKS.
4. CONSTRUCTORS MUST CHECK ALL DIMENSIONS FROM SITE.

REV.	DESCRIPTION	ISSUE DATE	INITIAL

DESIGN & DRAWN BY:
HENG THOURIN
LY VANPANHAPICH
TAING LEANGHOUT

PLOT DATE
12-Dec-24

SCALE
AS NOTED

REVISION


ISSUE STATUS
TD

PROJECT
SR VILLA

PROJECT NUMBER
016

DRAWING NAME
GF - GENERAL LAYOUT

DRAWING NUMBER
10-02

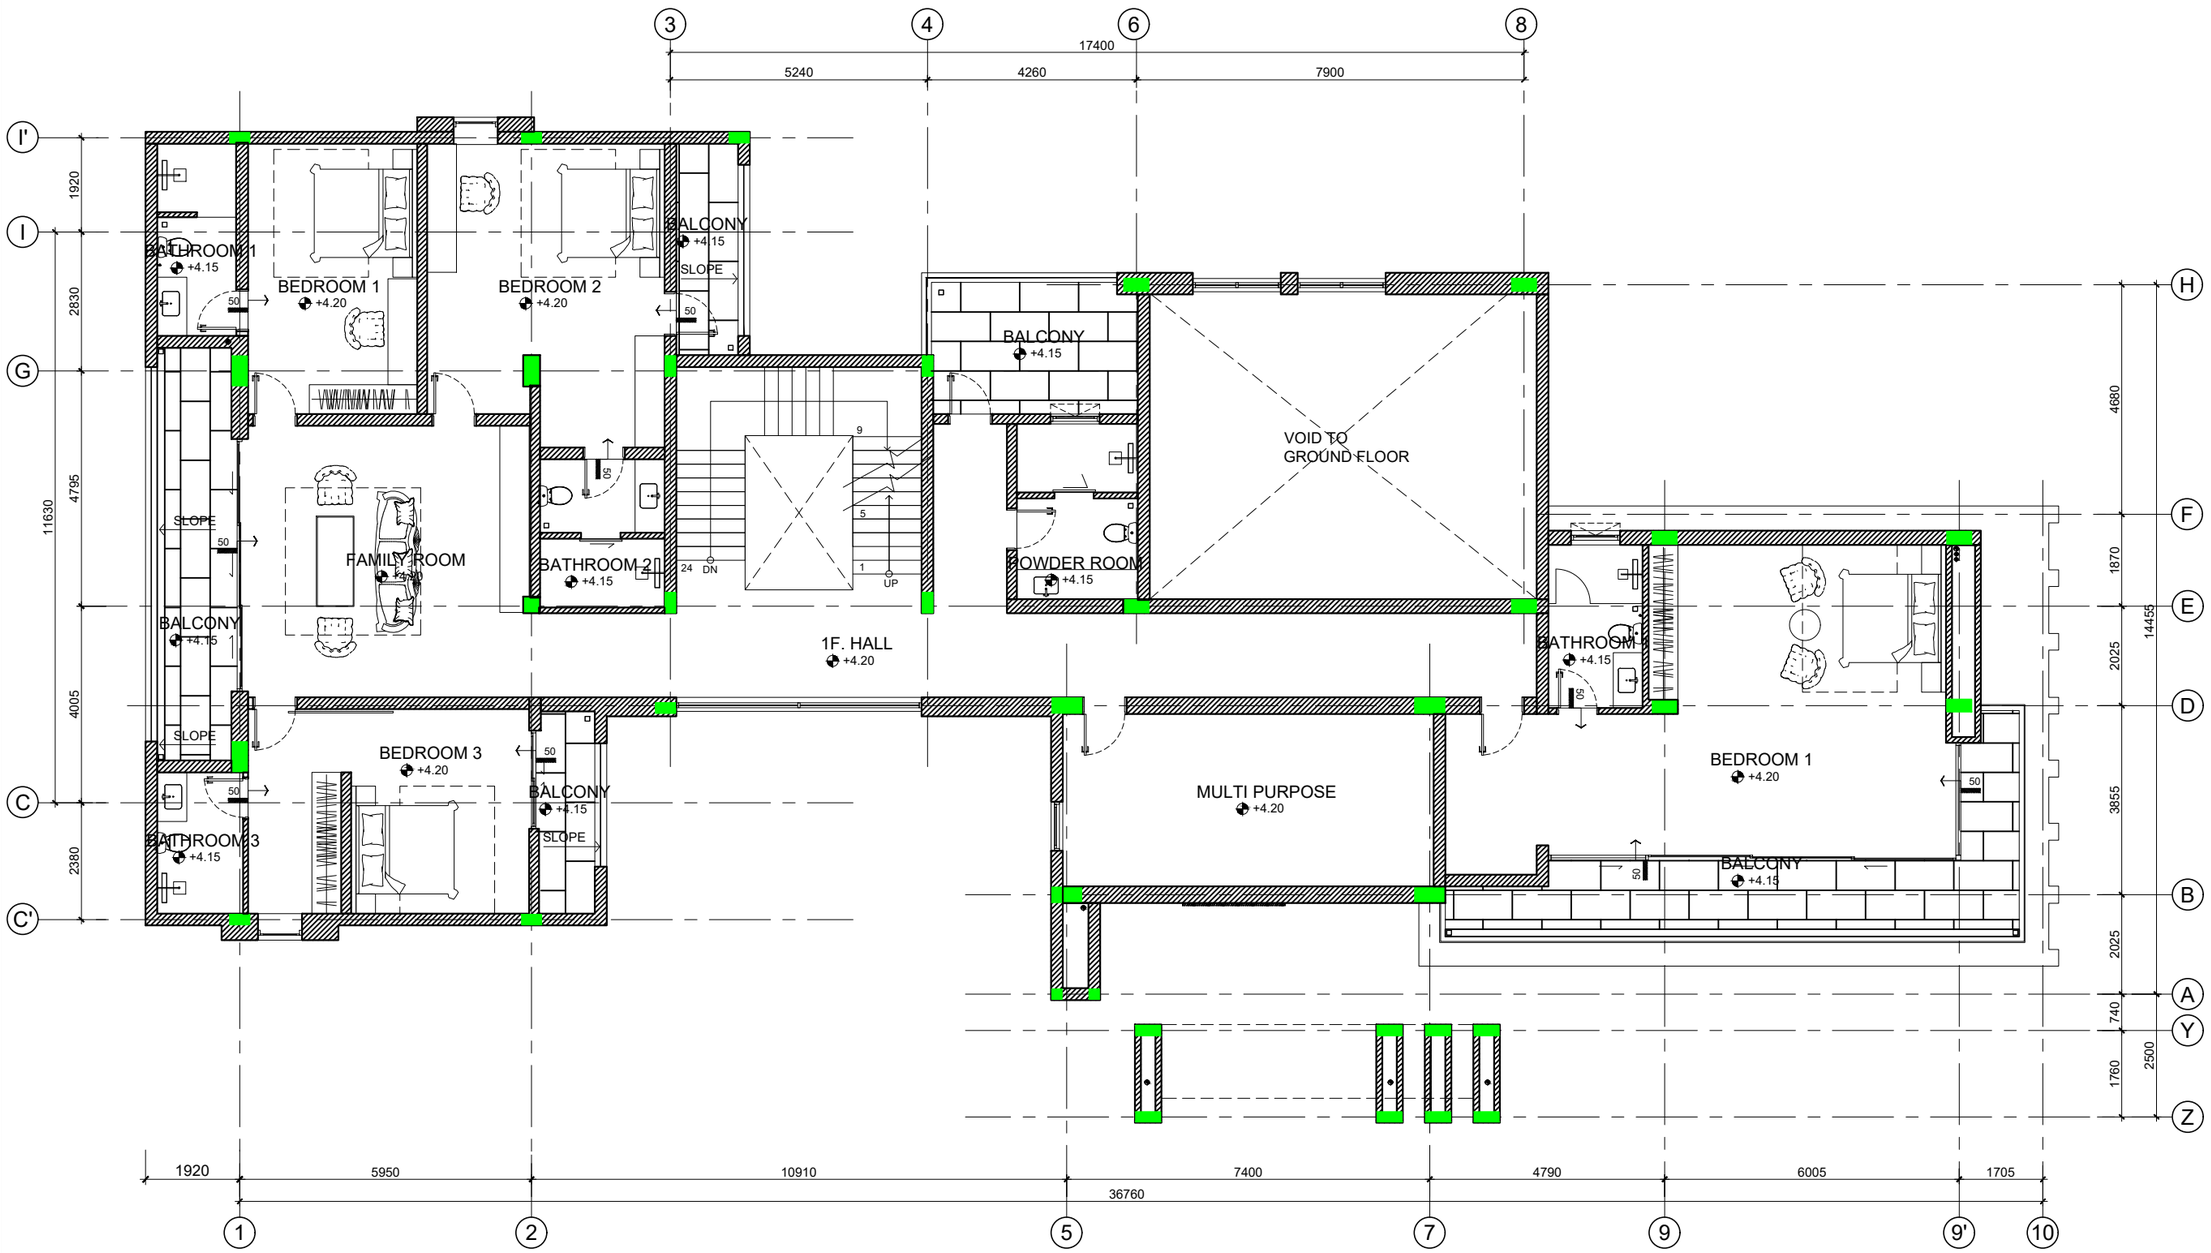

1 FIRST FLOOR PLAN
SCALE 1:125

TENDER
ISSUE
12-DEC-2024

PROJECT:
OWNER:

ADDRESS:
TEL. :

ARCHITECT

STRUCTURE ENGINEER

MEP ENGINEER

GENERAL NOTE:
1. THIS DRAWING AND ANY SPECIFICATION THAT MAY ACCOMPANY IT ARE THE PROPERTY OF THE ARCHITECT, ENGINEER AND/OR OTHER CONSULTANTS HEREWITH LISTED AND MUST NOT BE REPRODUCED IN ANY FORM, WHETHER IN WHOLE OR IN PART, WITHOUT THE EXPRESSED WRITTEN PERMISSION OF THE OWNERS.
2. ALL ARCHITECTURAL, STRUCTURAL, MECHANICAL/ELECTRICAL, INTERIOR, LANDSCAPE AND LIGHTING DESIGN DRAWINGS SHOWN ARE FOR DESIGN INTENT ONLY. CONTRACTOR TO PROVIDE DETAILED SHOP DRAWINGS FOR ARCHITECT'S AND/OR ENGINEER'S APPROVAL PRIOR TO CONSTRUCTION.
3. ON NO ACCOUNT MAY THIS DRAWINGS BE SCALED, ANY DISCREPANCY IN FIGURED DIMENSIONS (OR OTHERWISE DISCREPANCIES BETWEEN ARCHITECTURAL/STUCTURAL AND MECANICAL/ELECTRICAL DRAWINGS) IS TO BE REPORTED IMMEDIATELY TO THE ARCHITECT AND/OR ENGINEER BEFORE COMMENCEMENT OF WORKS.
4. CONSTRUCTORS MUST CHECK ALL DIMENSIONS FROM SITE.

REV.	DESCRIPTION	ISSUE DATE	INITIAL

DESIGN & DRAWN BY:
HENG THOURIN
LY VANPANHAPICH
TAING LEANGHOUT

PLOT DATE
12-Dec-24

SCALE
AS NOTED

REVISION


ISSUE STATUS
TD

PROJECT
SR VILLA

PROJECT NUMBER
016

DRAWING NAME
1F - GENERAL LAYOUT

DRAWING NUMBER
10-03

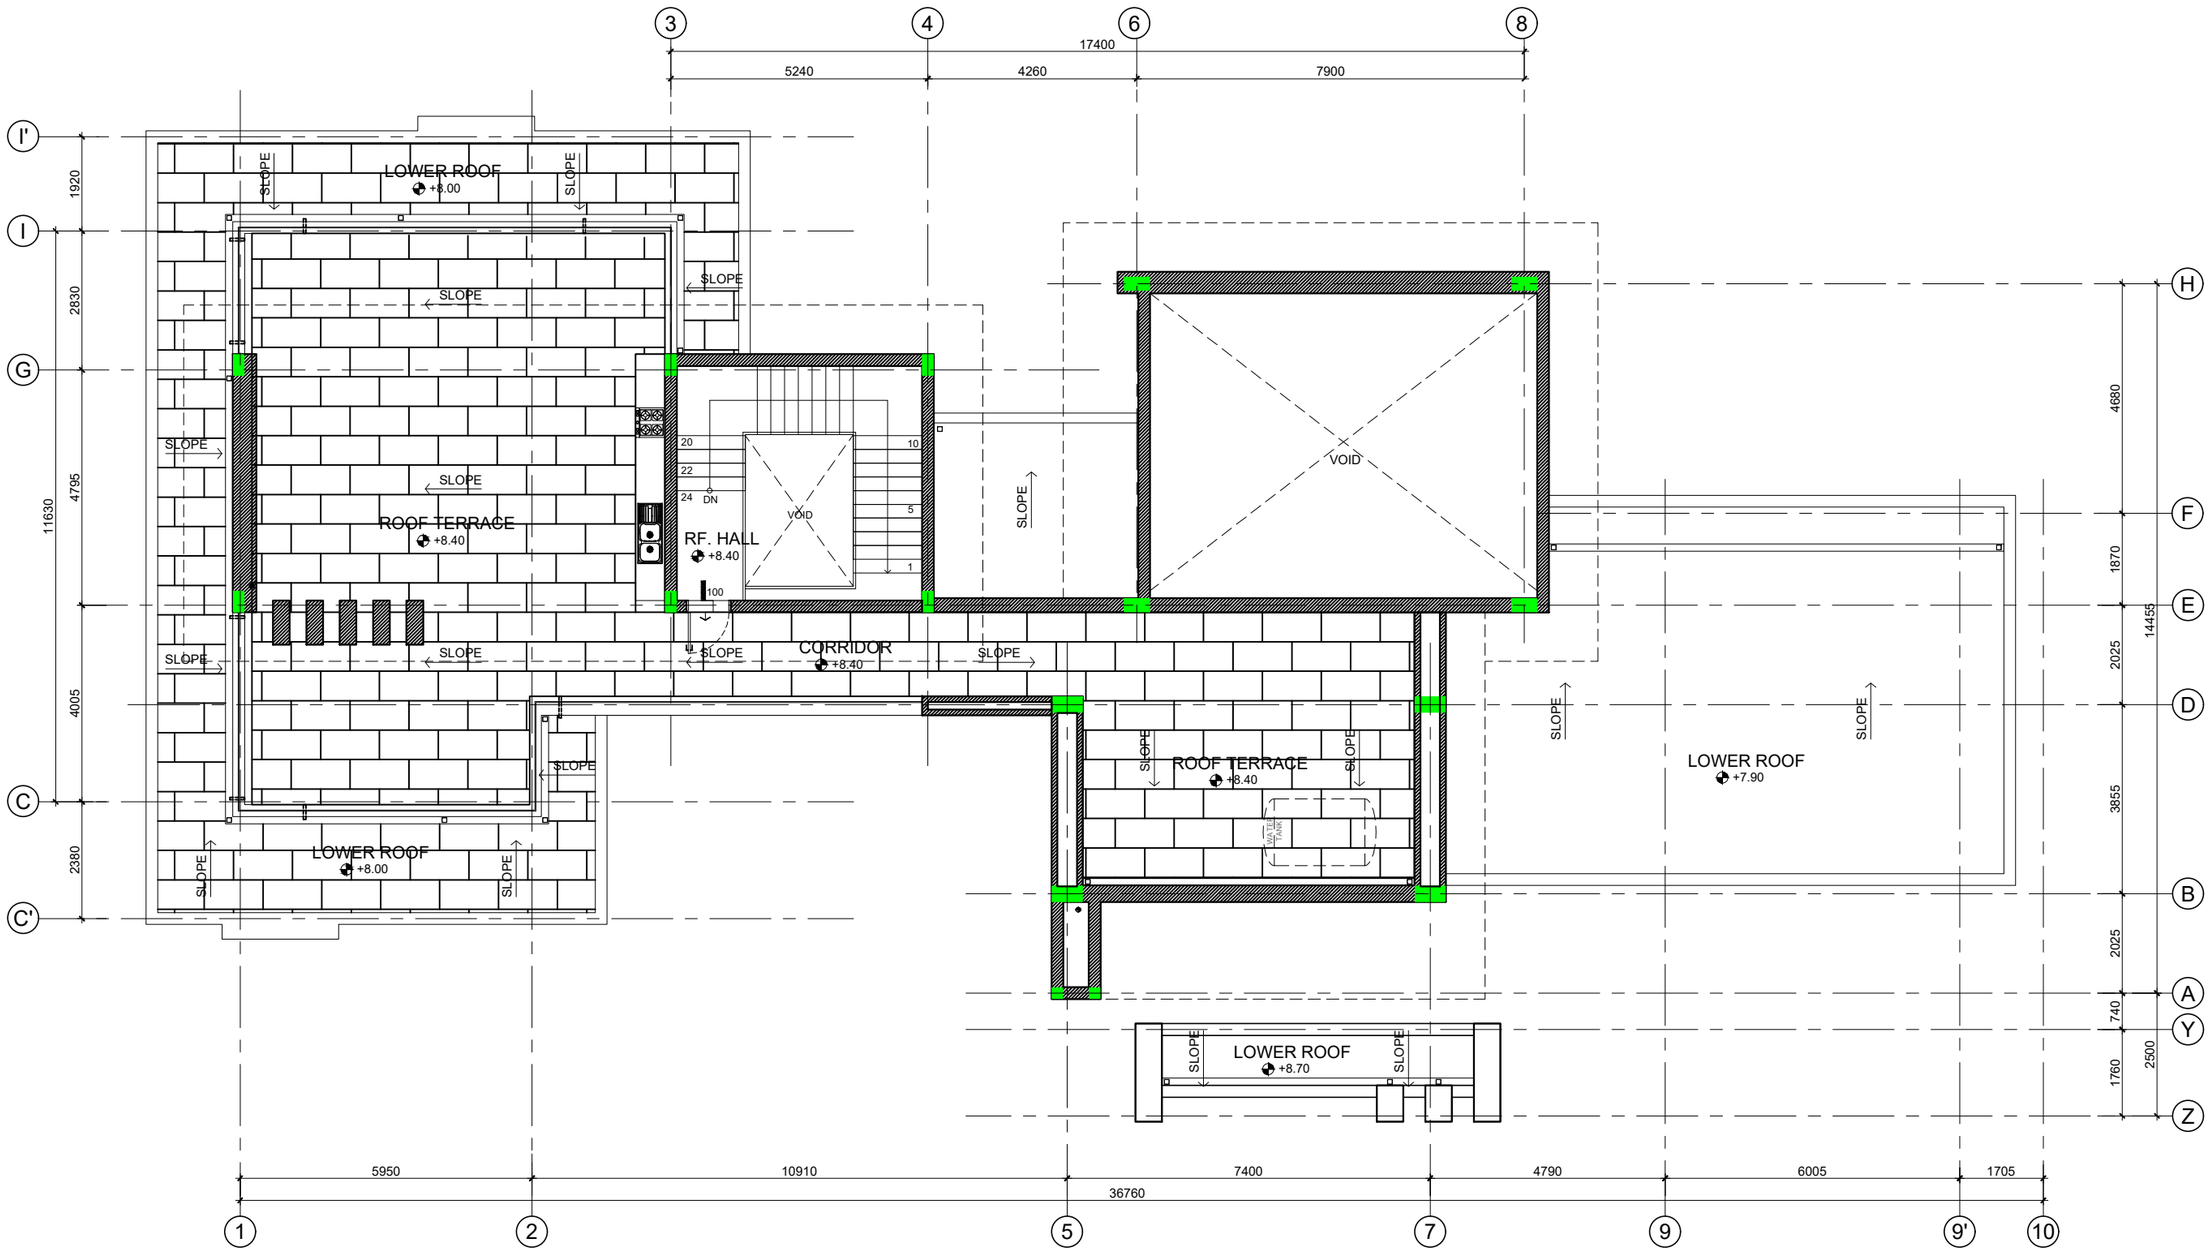

1 SECOND FLOOR PLAN
SCALE 1:125

TENDER
ISSUE
12-DEC-2024

PROJECT:
OWNER:

ADDRESS:
TEL. :

ARCHITECT

STRUCTURE ENGINEER

MEP ENGINEER


GENERAL NOTE:
1. THIS DRAWING AND ANY SPECIFICATION THAT MAY ACCOMPANY IT ARE THE PROPERTY OF THE ARCHITECT, ENGINEER AND/OR OTHER CONSULTANTS HEREWITH LISTED AND MUST NOT BE REPRODUCED IN ANY FORM, WHETHER IN WHOLE OR IN PART, WITHOUT THE EXPRESSED WRITTEN PERMISSION OF THE OWNERS.
2. ALL ARCHITECTURAL, STRUCTURAL, MECHANICAL/ELECTRICAL, INTERIOR, LANDSCAPE AND LIGHTING DESIGN DRAWINGS SHOWN ARE FOR DESIGN INTENT ONLY. CONTRACTOR TO PROVIDE DETAILED SHOP DRAWINGS FOR ARCHITECT'S AND/OR ENGINEER'S APPROVAL PRIOR TO CONSTRUCTION.
3. ON NO ACCOUNT MAY THIS DRAWINGS BE SCALED, ANY DISCREPANCY IN FIGURED DIMENSIONS (OR OTHERWISE DISCREPANCIES BETWEEN ARCHITECTURAL/STUCTURAL AND MECANICAL/ELECTRICAL DRAWINGS) IS TO BE REPORTED IMMEDIATELY TO THE ARCHITECT AND/OR ENGINEER BEFORE COMMENCEMENT OF WORKS.
4. CONSTRUCTORS MUST CHECK ALL DIMENSIONS FROM SITE.

REV.	DESCRIPTION	ISSUE DATE	INITIAL

DESIGN & DRAWN BY:	PLOT DATE
HENG THOURIN LY VANPANHAPICH TAING LEANGHOUT	12-Dec-24
SCALE *AS NOTED*	REVISION
ISSUE STATUS	TD
PROJECT	SR VILLA
PROJECT NUMBER	016

DRAWING NAME
2F - GENERAL LAYOUT

DRAWING NUMBER
10-04

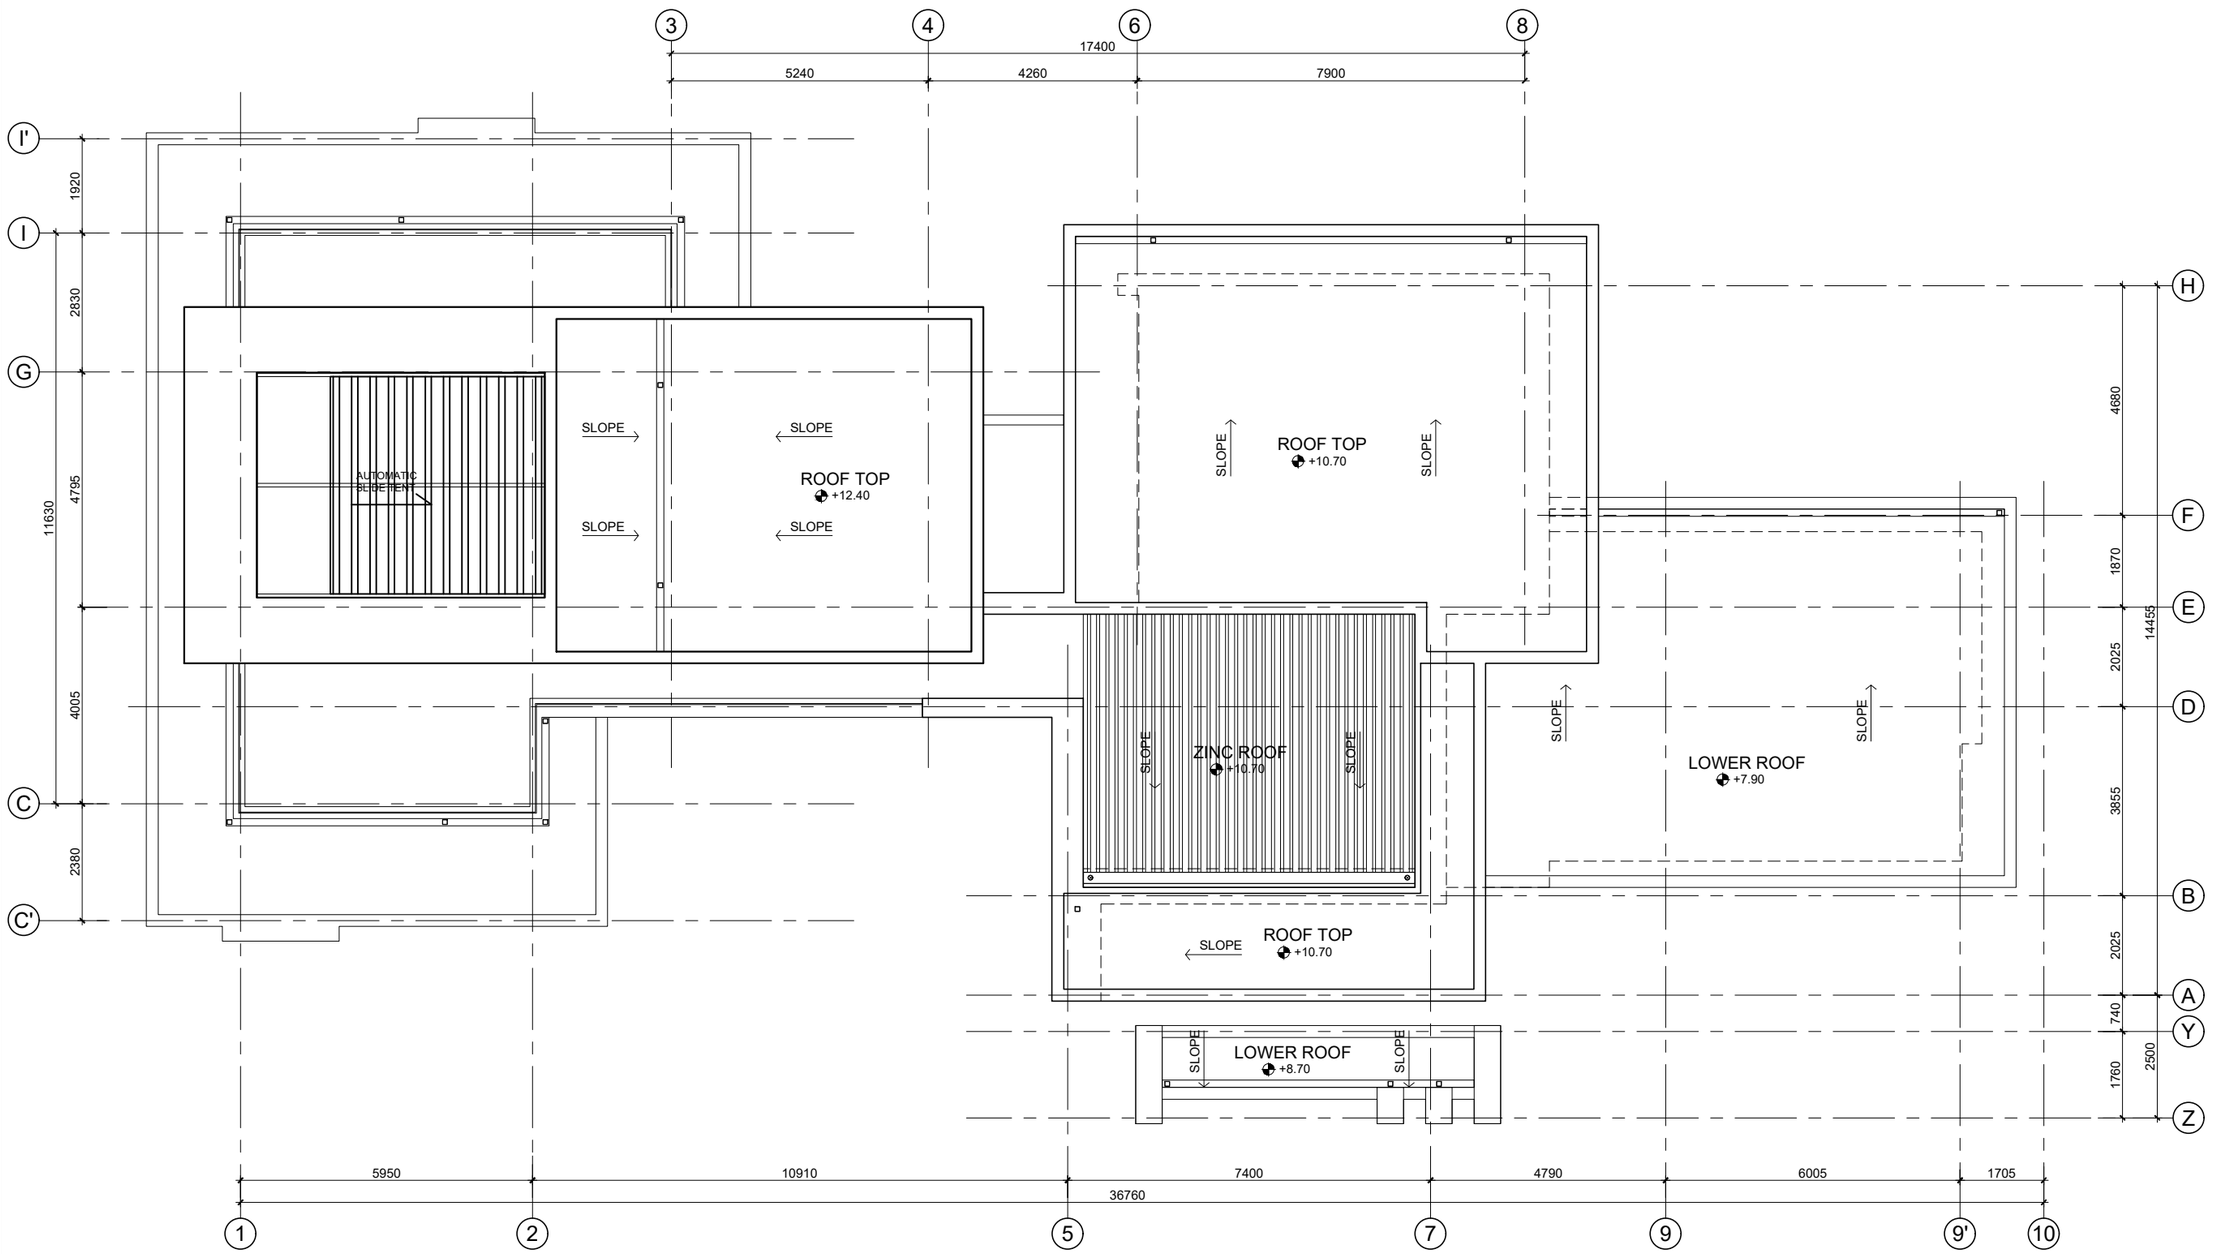

1 ROOF TOP PLAN
SCALE 1:125

TENDER
ISSUE
12-DEC-2024

PROJECT:
OWNER:

ADDRESS:
TEL. :

ARCHITECT

STRUCTURE ENGINEER

MEP ENGINEER


GENERAL NOTE:
1. THIS DRAWING AND ANY SPECIFICATION THAT MAY ACCOMPANY IT ARE THE PROPERTY OF THE ARCHITECT, ENGINEER AND/OR OTHER CONSULTANTS HEREWITH LISTED AND MUST NOT BE REPRODUCED IN ANY FORM, WHETHER IN WHOLE OR IN PART, WITHOUT THE EXPRESSED WRITTEN PERMISSION OF THE OWNERS.
2. ALL ARCHITECTURAL, STRUCTURAL, MECHANICAL/ELECTRICAL, INTERIOR, LANDSCAPE AND LIGHTING DESIGN DRAWINGS SHOWN ARE FOR DESIGN INTENT ONLY. CONTRACTOR TO PROVIDE DETAILED SHOP DRAWINGS FOR ARCHITECTS AND/OR ENGINEER'S APPROVAL PRIOR TO CONSTRUCTION.
3. ON NO ACCOUNT MAY THIS DRAWINGS BE SCALED, ANY DISCREPANCY IN FIGURED DIMENSIONS (OR OTHERWISE DISCREPANCIES BETWEEN ARCHITECTURAL/STUCTURAL AND MECANICAL/ELECTRICAL DRAWINGS) IS TO BE REPORTED IMMEDIATELY TO THE ARCHITECT AND/OR ENGINEER BEFORE COMMENCEMENT OF WORKS.
4. CONSTRUCTORS MUST CHECK ALL DIMENSIONS FROM SITE.

REV.	DESCRIPTION	ISSUE DATE	INITIAL


DESIGN & DRAWN BY:	PLOT DATE
HENG THOURIN	12-Dec-24
LY VANPANHAPICH	SCALE: AS NOTED / REVISION
TAING LEANGHOUT	ISSUE STATUS: TD
PROJECT: SR VILLA	PROJECT NUMBER: 016

DRAWING NAME
ROOFTOP - GENERAL LAYOUT

DRAWING NUMBER
10-05

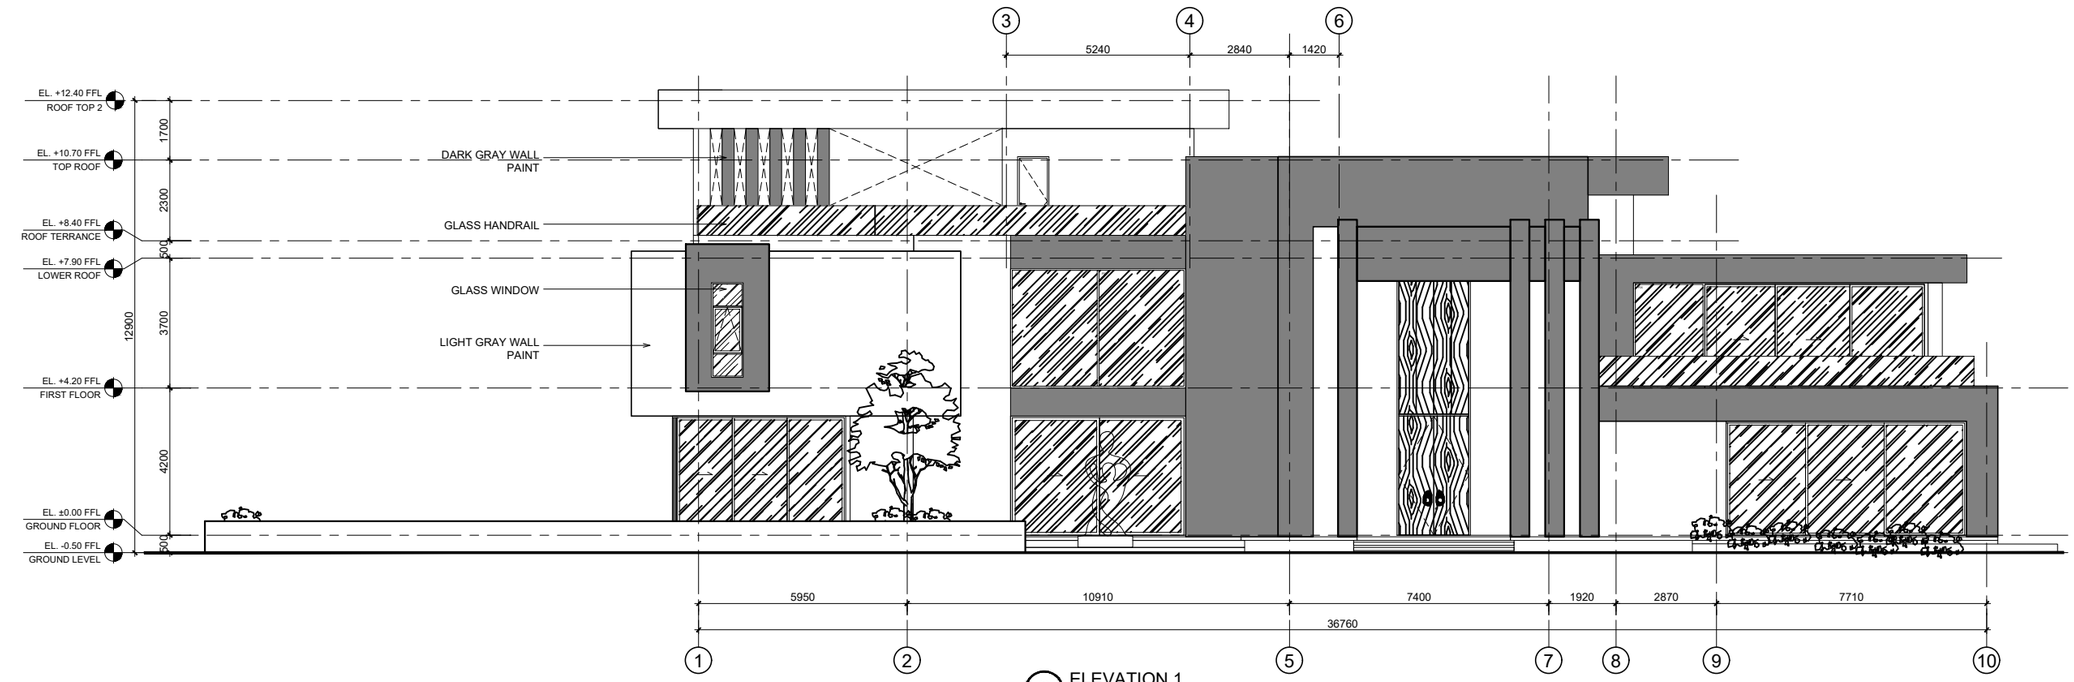

2 ELEVATION 1
SCALE 1:175

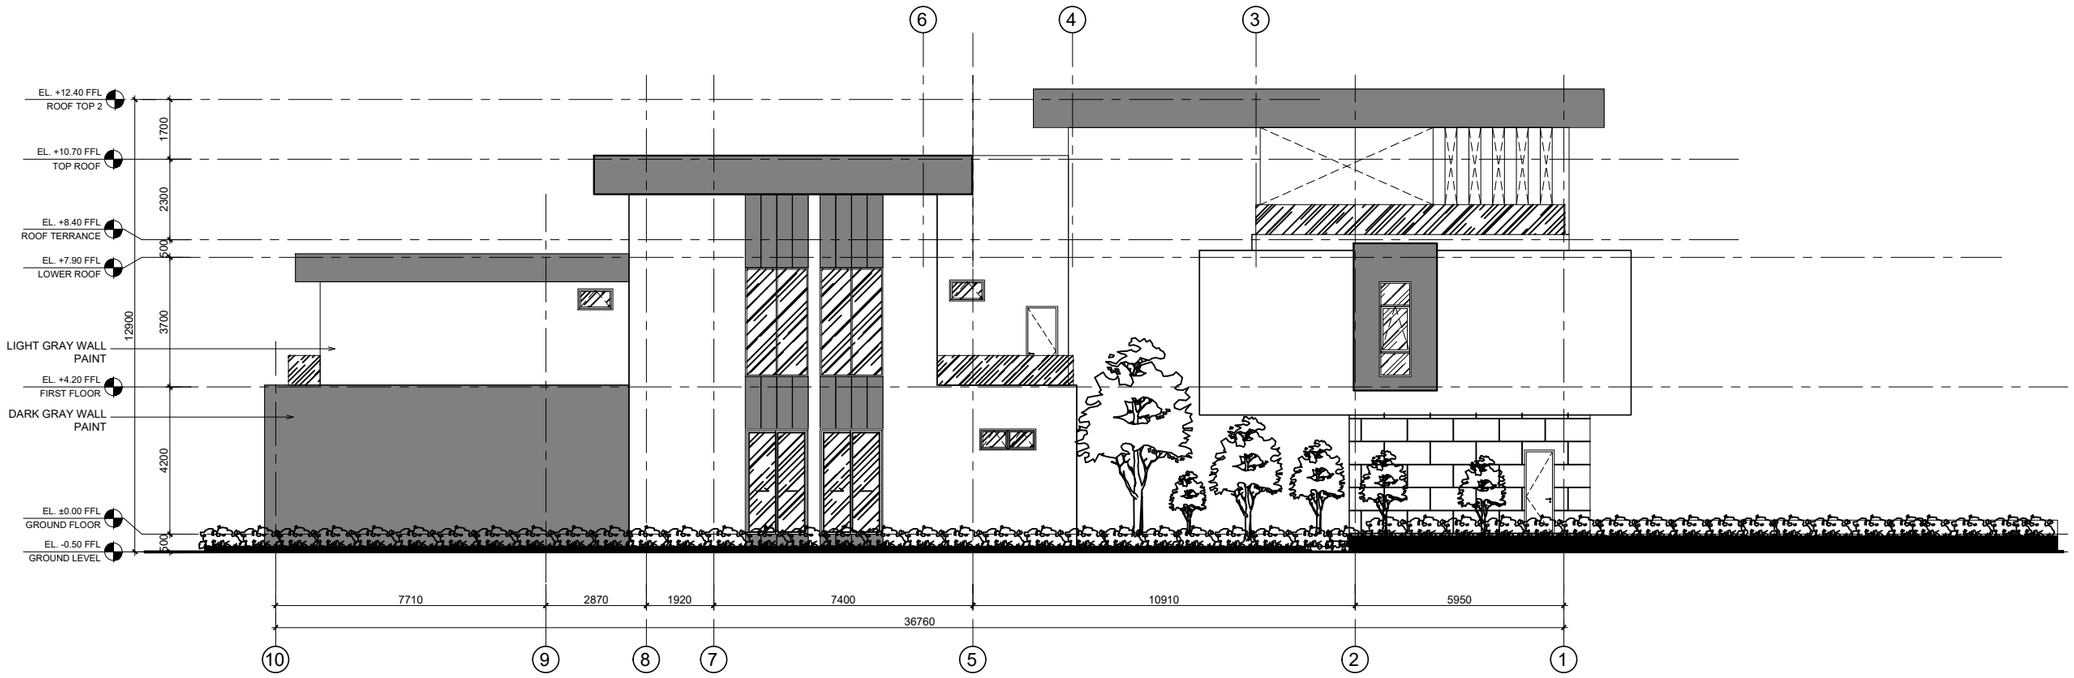

2 ELEVATION 2
SCALE 1:175

TENDER
ISSUE
12-DEC-2024

PROJECT:
OWNER:

ADDRESS:
TEL. :

ARCHITECT

STRUCTURE ENGINEER

MEP ENGINEER

GENERAL NOTE:
1. THIS DRAWING AND ANY SPECIFICATION THAT MAY ACCOMPANY IT ARE THE PROPERTY OF THE ARCHITECT, ENGINEER AND/OR OTHER CONSULTANTS HEREWITH LISTED AND MUST NOT BE REPRODUCED IN ANY FORM, WHETHER IN WHOLE OR IN PART, WITHOUT THE EXPRESSED WRITTEN PERMISSION OF THE OWNERS.
2. ALL ARCHITECTURAL, STRUCTURAL, MECHANICAL/ELECTRICAL, INTERIOR, LANDSCAPE AND LIGHTING DESIGN DRAWINGS SHOWN ARE FOR DESIGN INTENT ONLY. CONTRACTOR TO PROVIDE DETAILED SHOP DRAWINGS FOR ARCHITECT'S AND/OR ENGINEER'S APPROVAL PRIOR TO CONSTRUCTION.
3. ON NO ACCOUNT MAY THIS DRAWINGS BE SCALED, ANY DISCREPANCY IN FIGURED DIMENSIONS (OR OTHERWISE DISCREPANCIES BETWEEN ARCHITECTURAL/STUCTURAL AND MECANICAL/ELECTRICAL DRAWINGS) IS TO BE REPORTED IMMEDIATELY TO THE ARCHITECT AND/OR ENGINEER BEFORE COMMENCEMENT OF WORKS.
4. CONSTRUCTORS MUST CHECK ALL DIMENSIONS FROM SITE.

REV.	DESCRIPTION	ISSUE DATE	INITIAL

DESIGN & DRAWN BY:
HENG THOURIN
LY VANPANHAPICH
TAING LEANGHOUT

PLOT DATE
12-Dec-24

SCALE
AS NOTED

REVISION


ISSUE STATUS
TD

PROJECT
SR VILLA


PROJECT NUMBER
016

DRAWING NAME
ELEVATION 1 2

DRAWING NUMBER
11-01

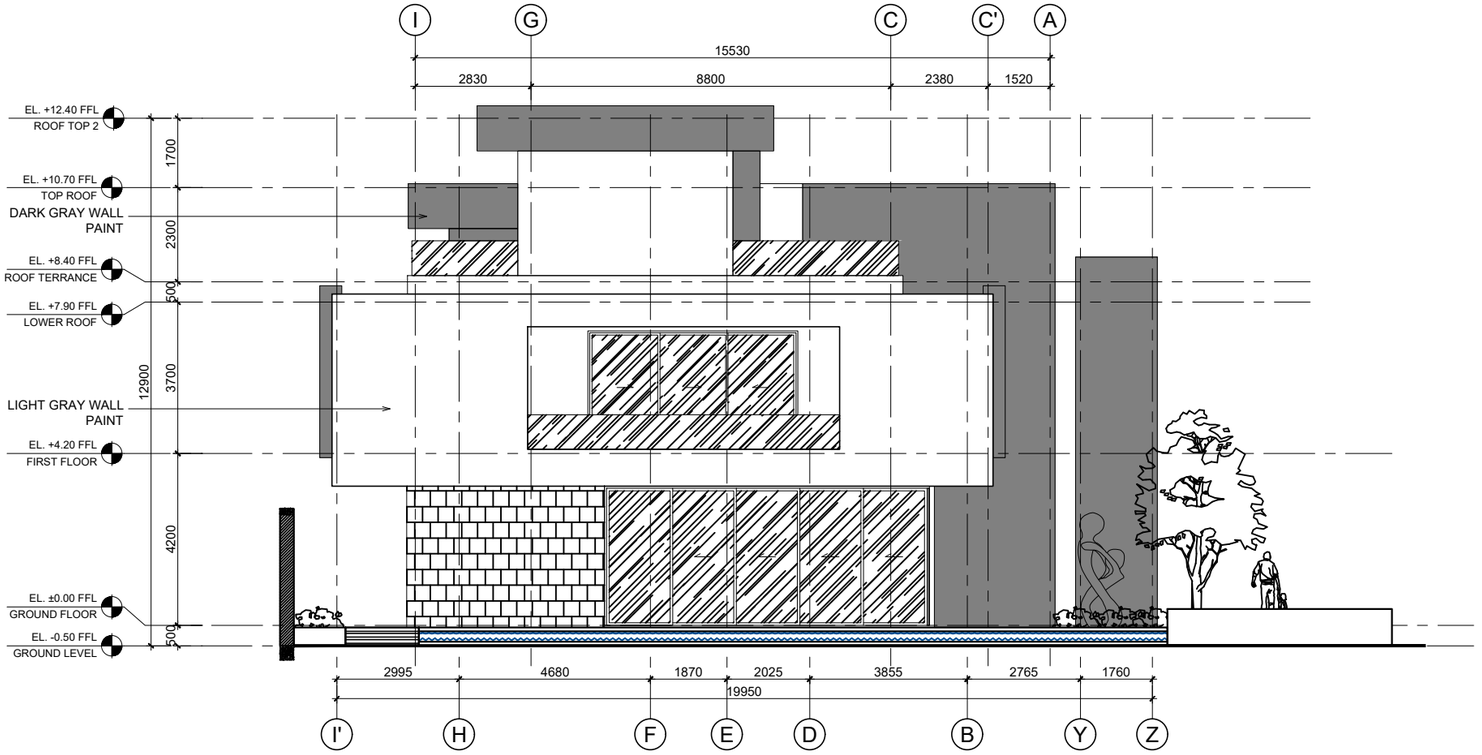

1 ELEVATION 3
SCALE 1:150

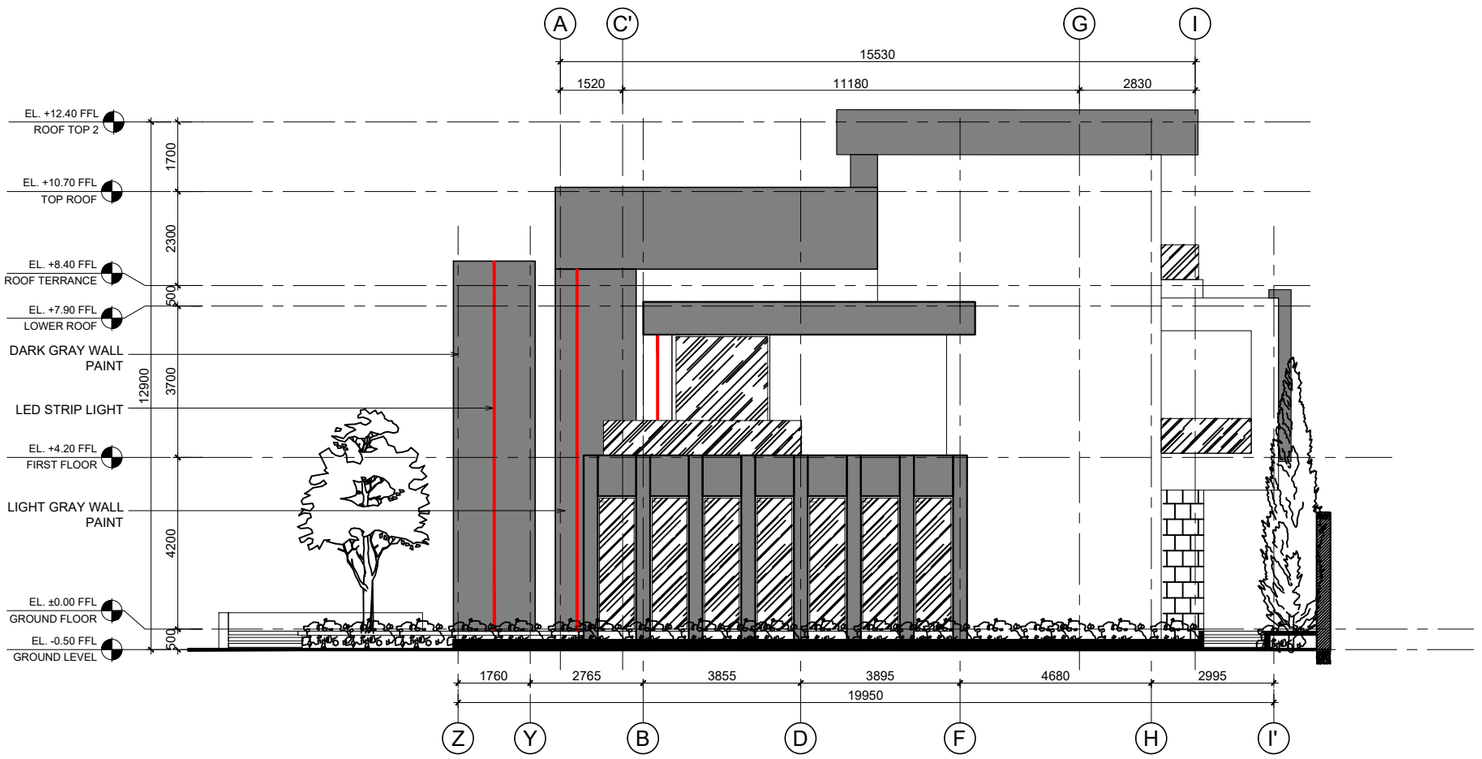

2 ELEVATION 4
SCALE 1:150

TENDER
ISSUE
12-DEC-2024

PROJECT:
OWNER:

ADDRESS:
TEL. :

ARCHITECT

STRUCTURE ENGINEER

MEP ENGINEER

GENERAL NOTE:
1. THIS DRAWING AND ANY SPECIFICATION THAT MAY ACCOMPANY IT ARE THE PROPERTY OF THE ARCHITECT, ENGINEER AND/OR OTHER CONSULTANTS HEREWITH LISTED AND MUST NOT BE REPRODUCED IN ANY FORM, WHETHER IN WHOLE OR IN PART, WITHOUT THE EXPRESSED WRITTEN PERMISSION OF THE OWNERS.
2. ALL ARCHITECTURAL, STRUCTURAL, MECHANICAL/ELECTRICAL, INTERIOR, LANDSCAPE AND LIGHTING DESIGN DRAWINGS SHOWN ARE FOR DESIGN INTENT ONLY. CONTRACTOR TO PROVIDE DETAILED SHOP DRAWINGS FOR ARCHITECT'S AND/OR ENGINEER'S APPROVAL PRIOR TO CONSTRUCTION.
3. ON NO ACCOUNT MAY THIS DRAWINGS BE SCALED, ANY DISCREPANCY IN FIGURED DIMENSIONS (OR OTHERWISE DISCREPANCIES BETWEEN ARCHITECTURAL/STUCTURAL AND MECANICAL/ELECTRICAL DRAWINGS) IS TO BE REPORTED IMMEDIATELY TO THE ARCHITECT AND/OR ENGINEER BEFORE COMMENCEMENT OF WORKS.
4. CONSTRUCTORS MUST CHECK ALL DIMENSIONS FROM SITE.

REV.	DESCRIPTION	ISSUE DATE	INITIAL

DESIGN & DRAWN BY:
HENG THOURIN
LY VANPANHAPICH
TAING LEANGHOUT

PLOT DATE
12-Dec-24

SCALE
AS NOTED

REVISION


ISSUE STATUS
TD

PROJECT
SR VILLA


PROJECT NUMBER
016

DRAWING NAME
ELEVATION 3 4

DRAWING NUMBER
11-02

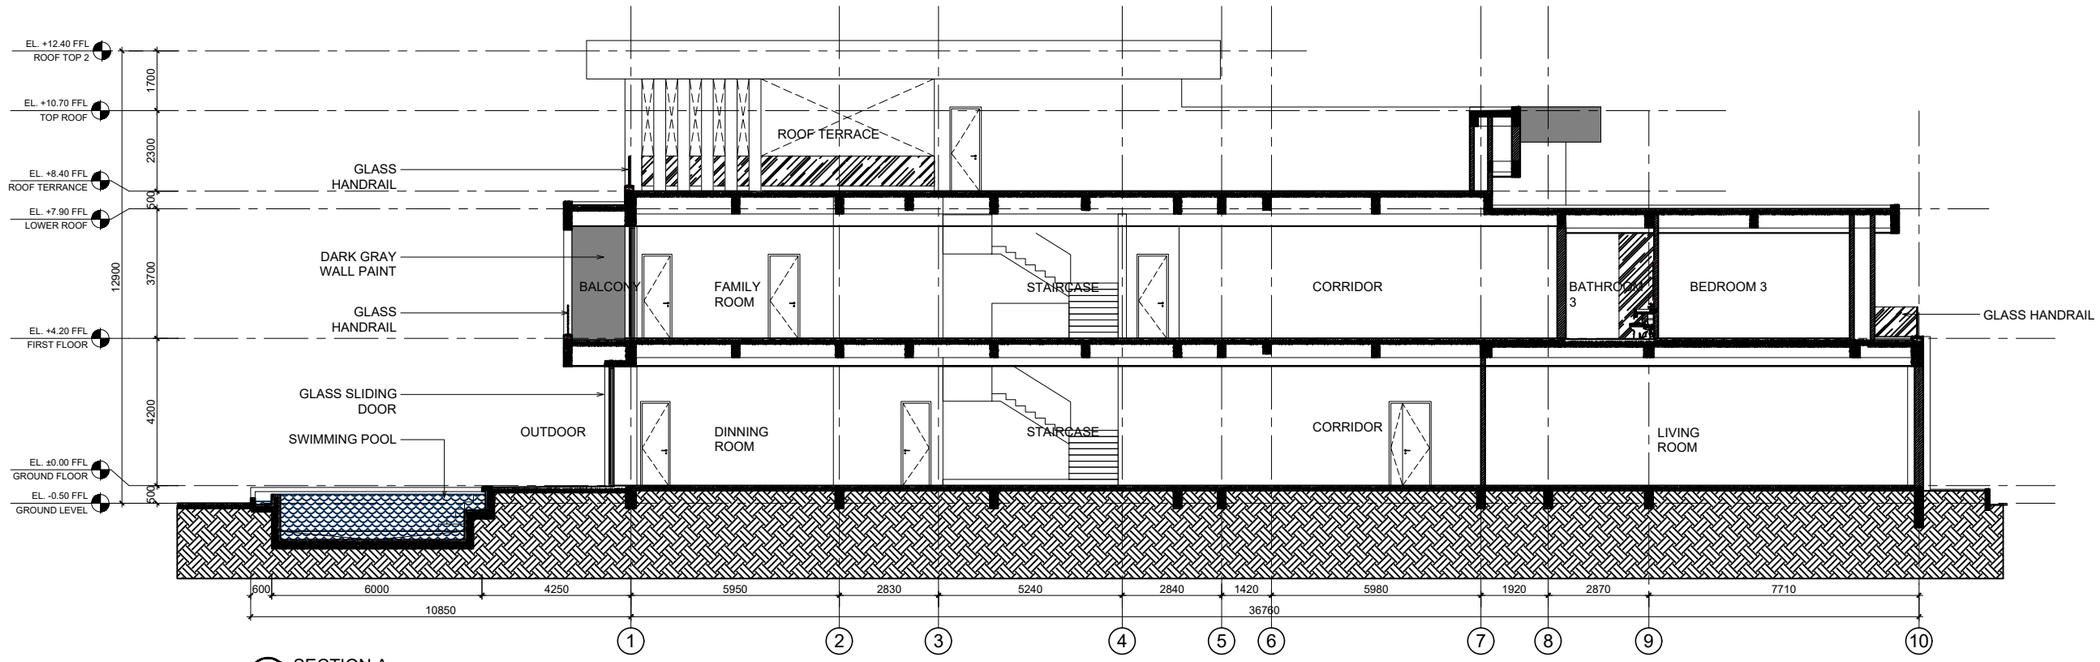

1 SECTION A
SCALE 1:175

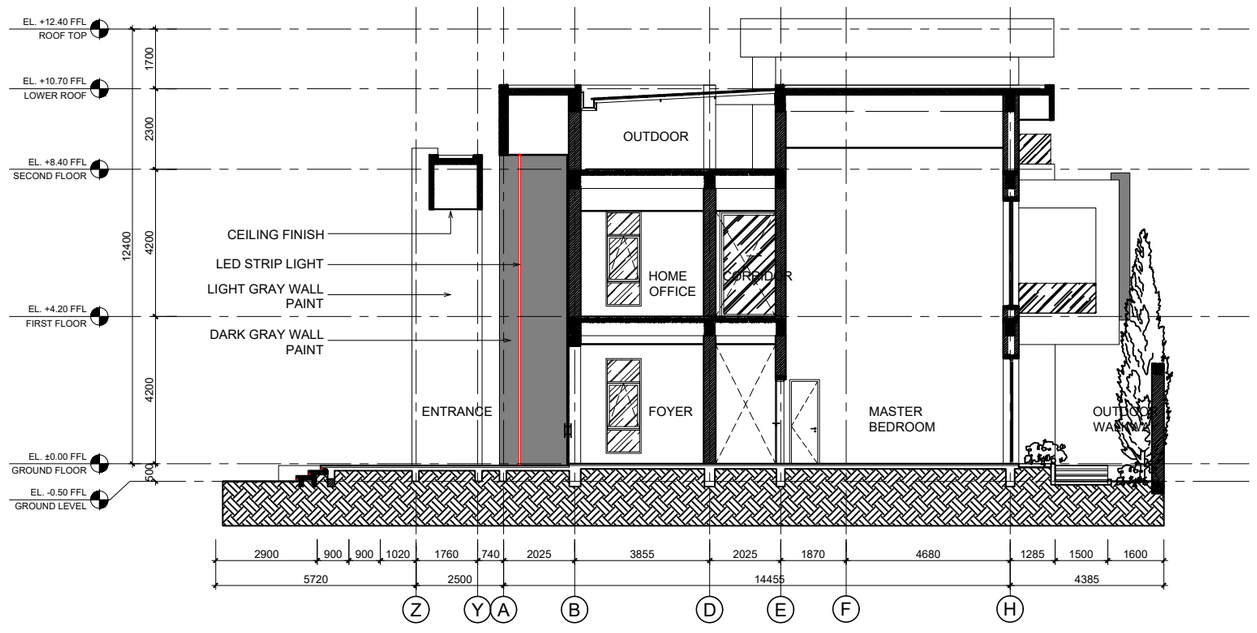

2 SECTION B
SCALE 1:175

TENDER
ISSUE
12-DEC-2024

PROJECT:
OWNER:

ADDRESS:
TEL. :

ARCHITECT

STRUCTURE ENGINEER

MEP ENGINEER

GENERAL NOTE:
1. THIS DRAWING AND ANY SPECIFICATION THAT MAY ACCOMPANY IT ARE THE PROPERTY OF THE ARCHITECT, ENGINEER AND/OR OTHER CONSULTANTS HEREWITH LISTED AND MUST NOT BE REPRODUCED IN ANY FORM, WHETHER IN WHOLE OR IN PART, WITHOUT THE EXPRESSED WRITTEN PERMISSION OF THE OWNERS.
2. ALL ARCHITECTURAL, STRUCTURAL, MECHANICAL/ELECTRICAL, INTERIOR, LANDSCAPE AND LIGHTING DESIGN DRAWINGS SHOWN ARE FOR DESIGN INTENT ONLY. CONTRACTOR TO PROVIDE DETAILED SHOP DRAWINGS FOR ARCHITECT'S AND/OR ENGINEER'S APPROVAL PRIOR TO CONSTRUCTION.
3. ON NO ACCOUNT MAY THIS DRAWINGS BE SCALED, ANY DISCREPANCY IN FIGURED DIMENSIONS (OR OTHERWISE DISCREPANCIES BETWEEN ARCHITECTURAL/STUCTURAL AND MECANICAL/ELECTRICAL DRAWINGS) IS TO BE REPORTED IMMEDIATELY TO THE ARCHITECT AND/OR ENGINEER BEFORE COMMENCEMENT OF WORKS.
4. CONSTRUCTORS MUST CHECK ALL DIMENSIONS FROM SITE.

REV.	DESCRIPTION	ISSUE DATE	INITIAL

DESIGN & DRAWN BY:
HENG THOURIN
LY VANPANHAPICH
TAING LEANGHOUT

PLOT DATE
12-Dec-24

SCALE
AS NOTED

REVISION

ISSUE STATUS
TD

PROJECT
SR VILLA

PROJECT NUMBER
016

DRAWING NAME
SECTION A B

DRAWING NUMBER
12-01